



涵洞组成

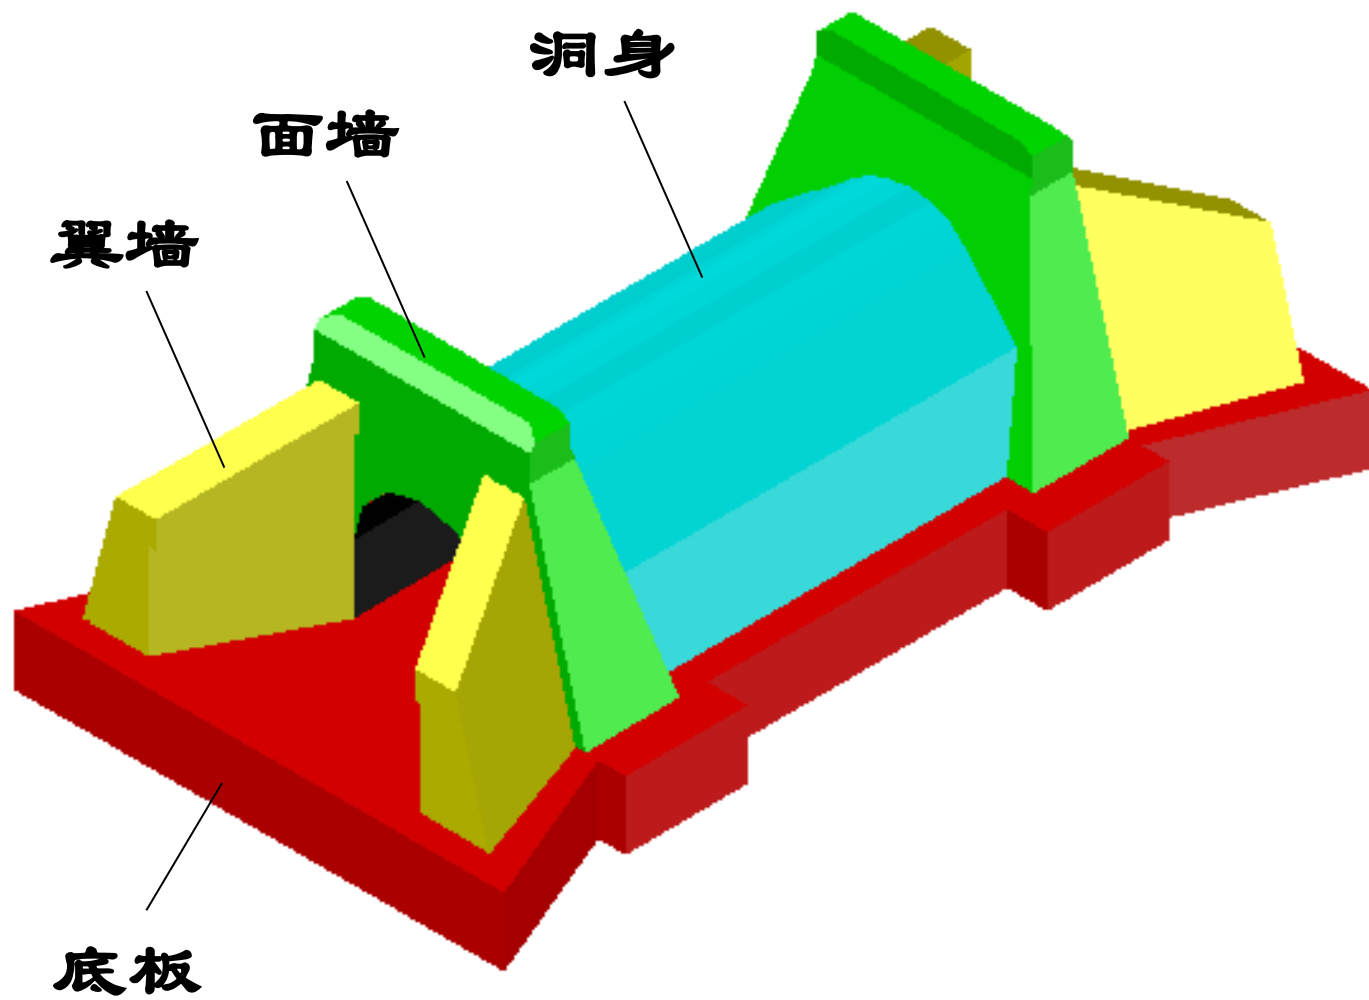

1、底板

整个结构的最下面部分，可看作由长方体切割而成，其长度贯穿全洞。

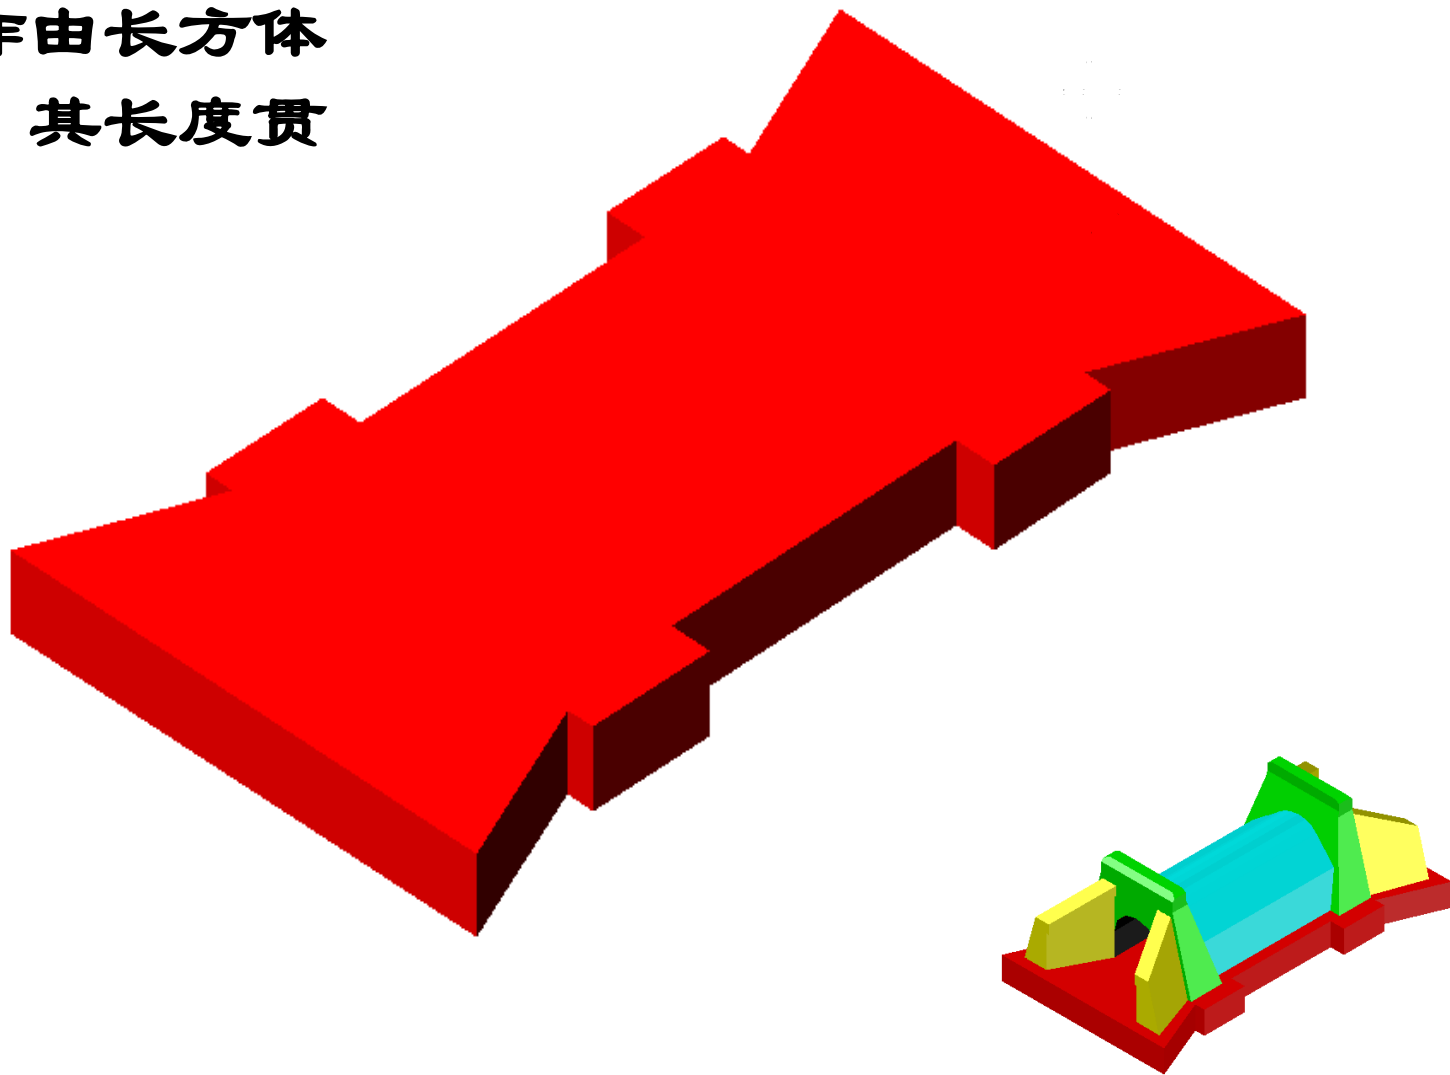


(注意: 图中 $AB \parallel CD$)

(注意: 图中 $AB \parallel CD$)



(注意: 图中 $AB \parallel CD$)


(注意: 图中 $AB \parallel CD$)

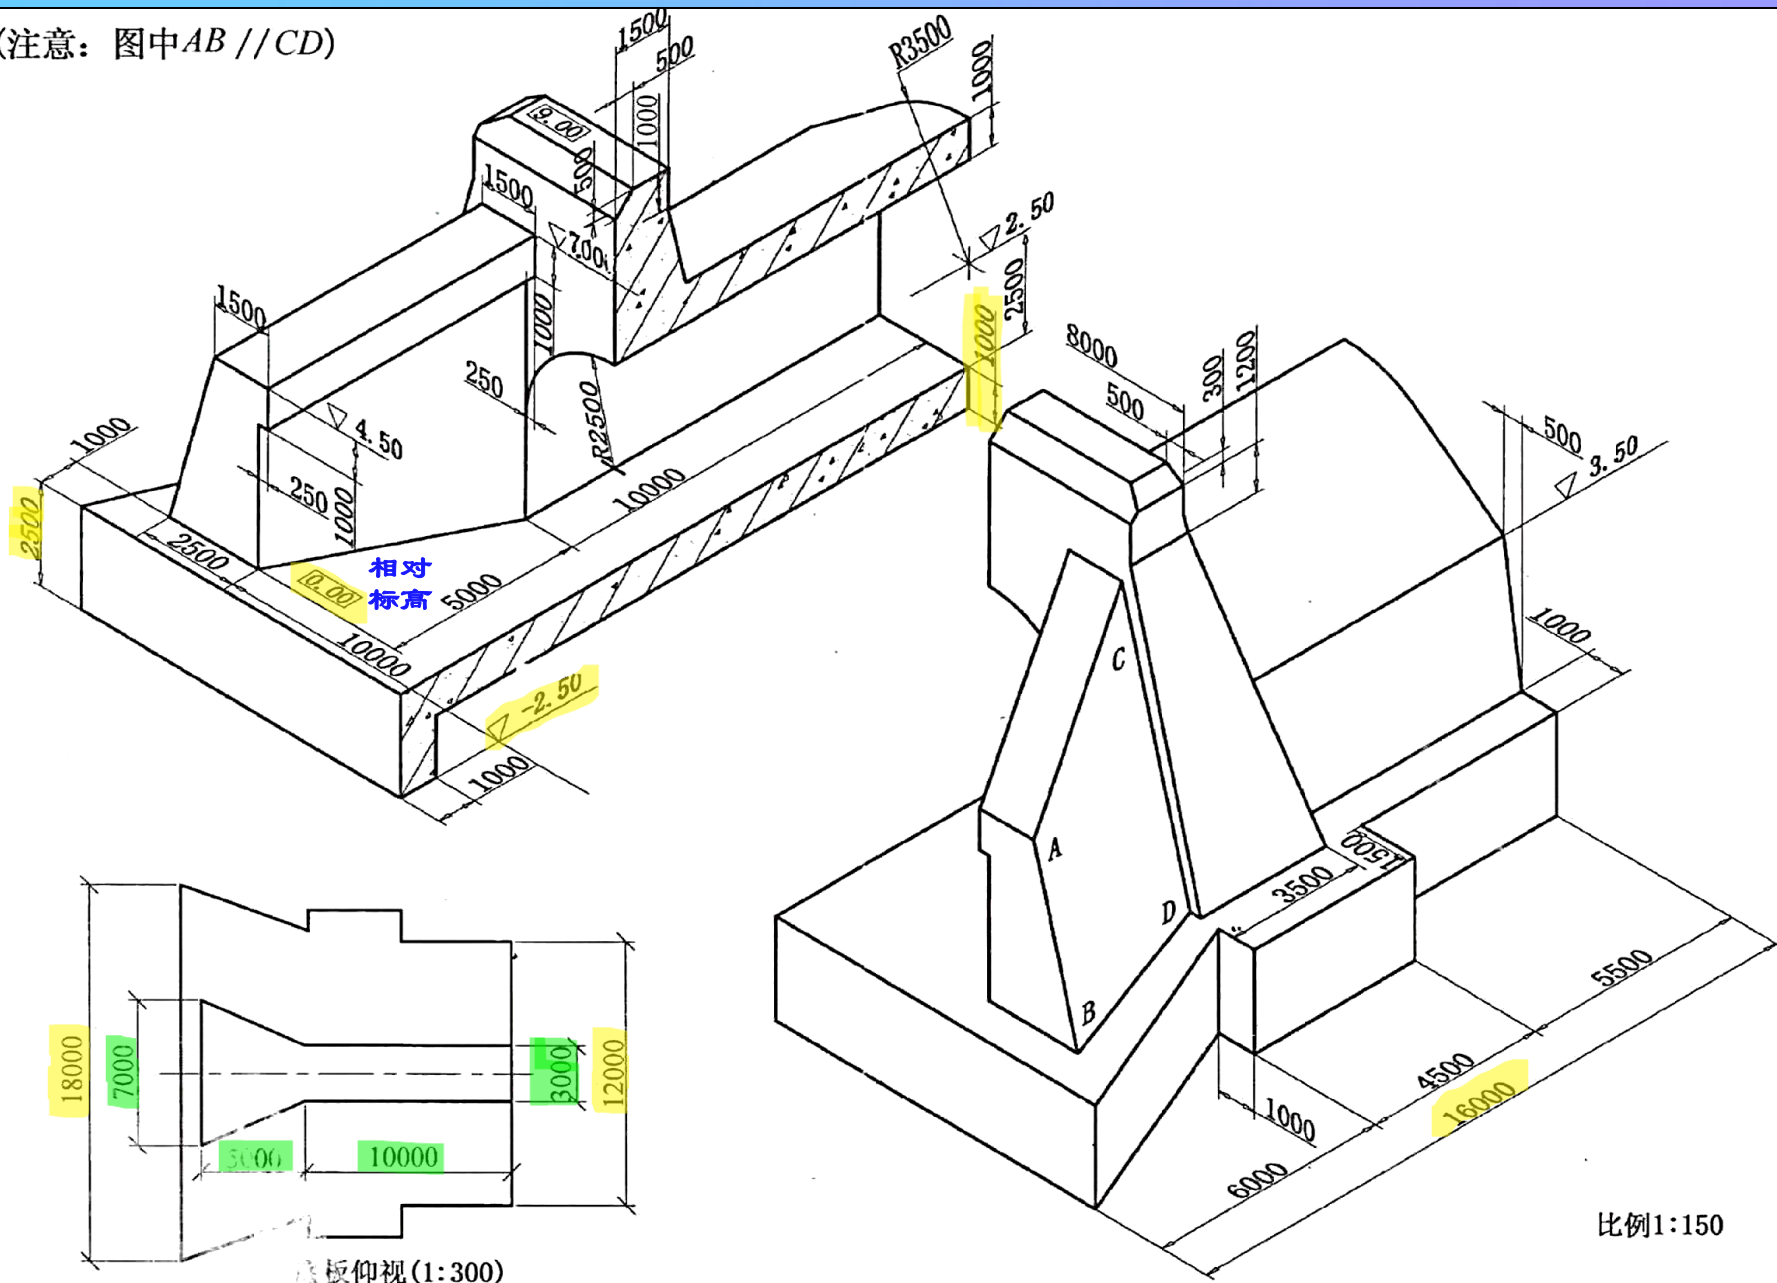

比例1:150


底板的尺寸

注意：底板底面中间部分为燕尾形空槽

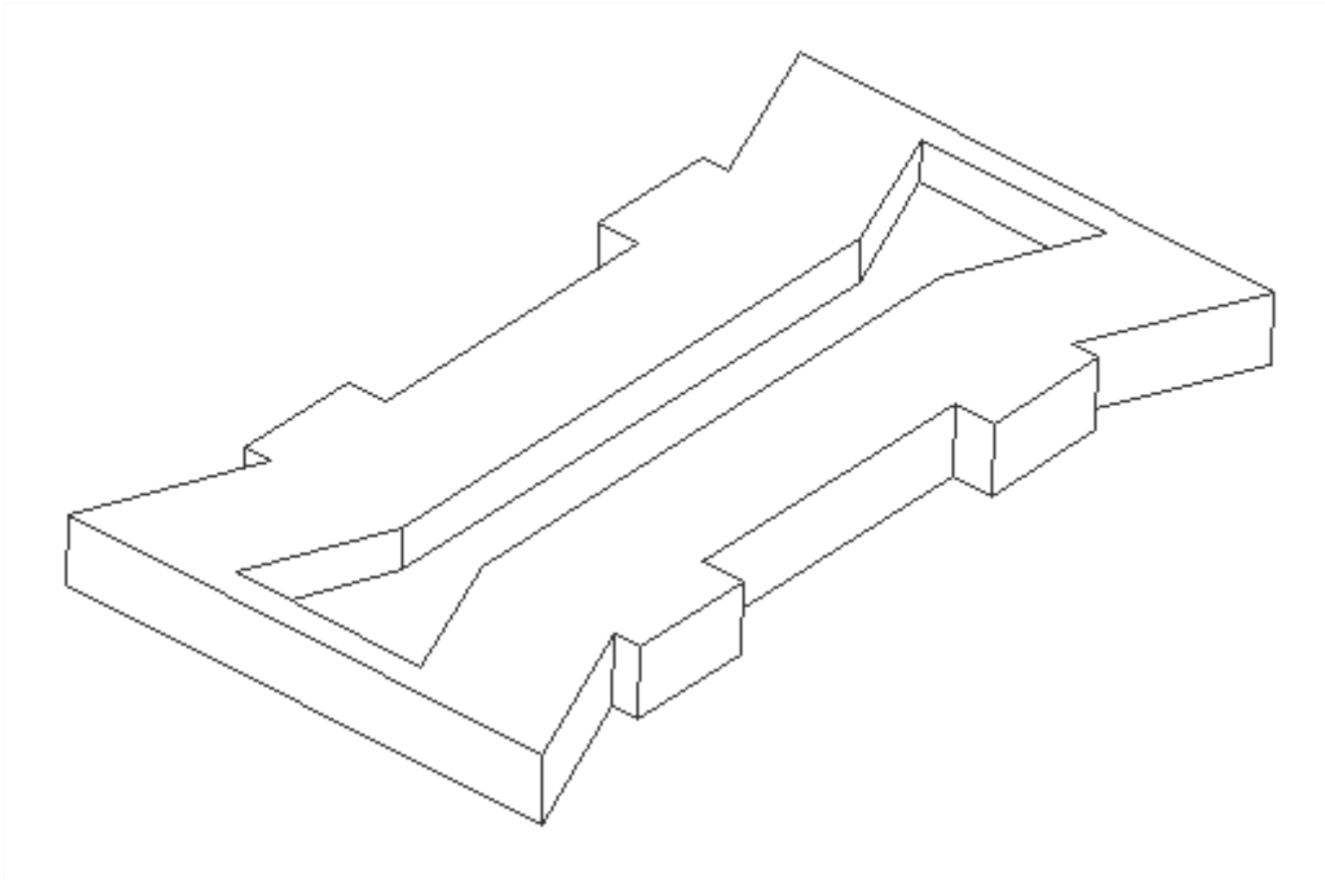


2、翼墙

翼墙是洞口两侧的挡土墙，呈八字形。

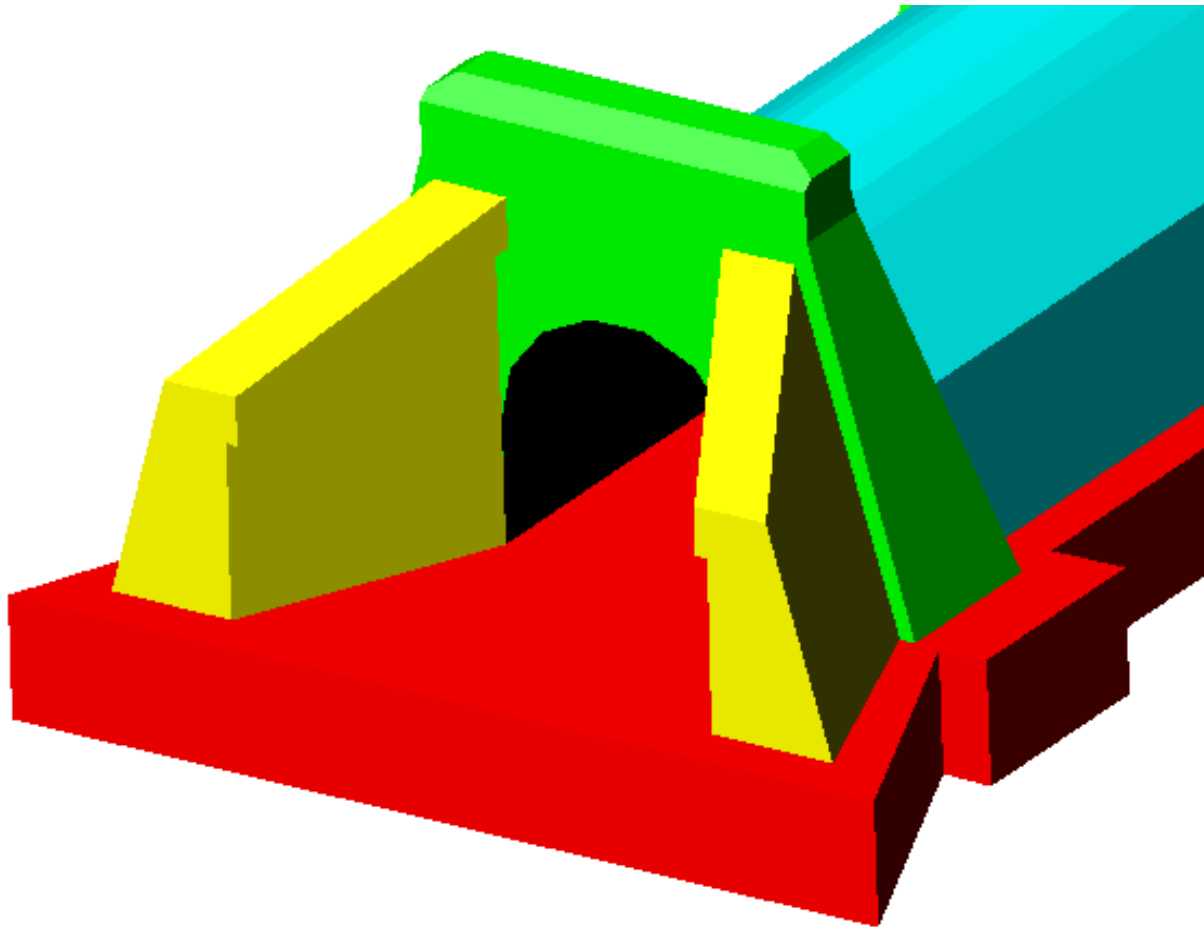


(注意: 图中 $AB \parallel CD$)

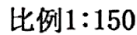


3、面墙

翼墙后面直立部分即为面墙，可看作由长方体切割并穿孔而成。

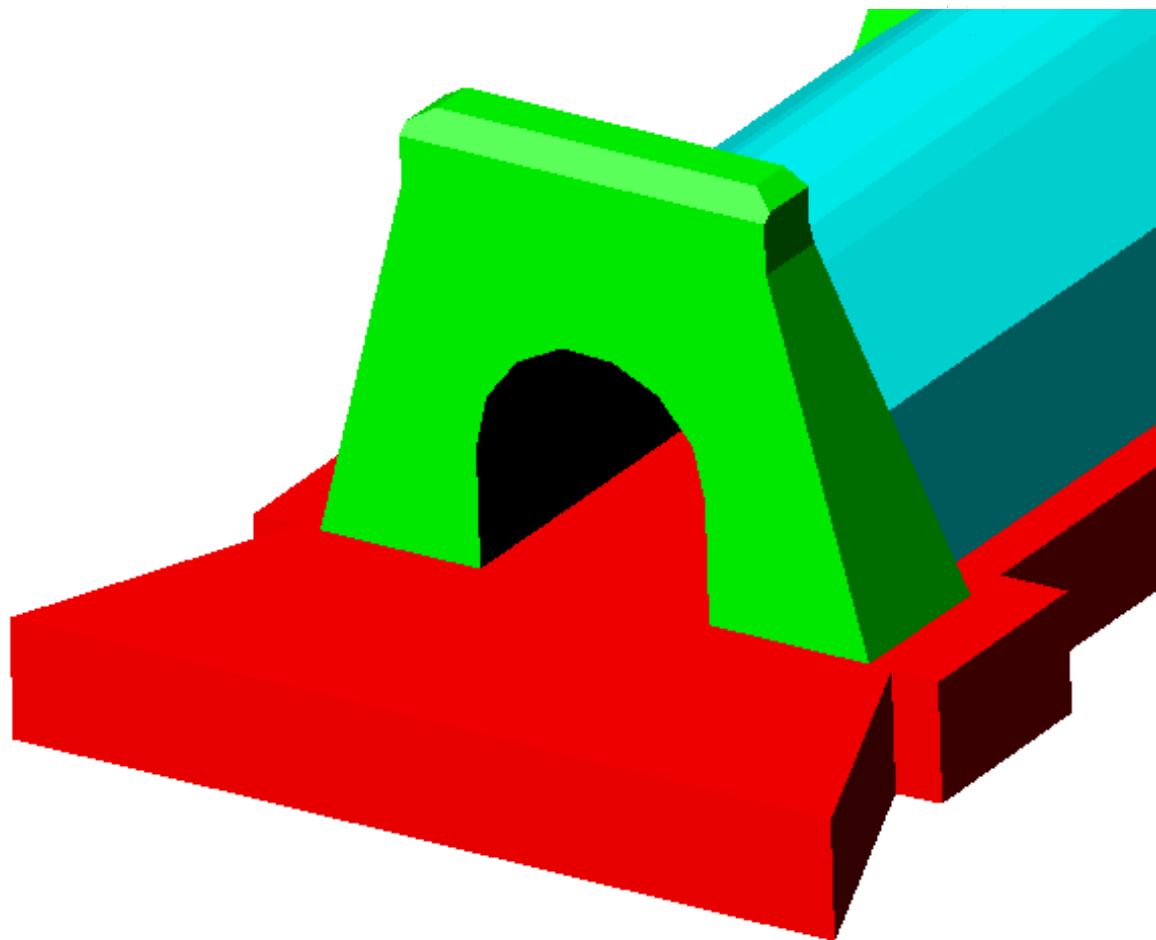

(注意: 图中 $AB \parallel CD$)


(注意: 图中 $AB \parallel CD$)

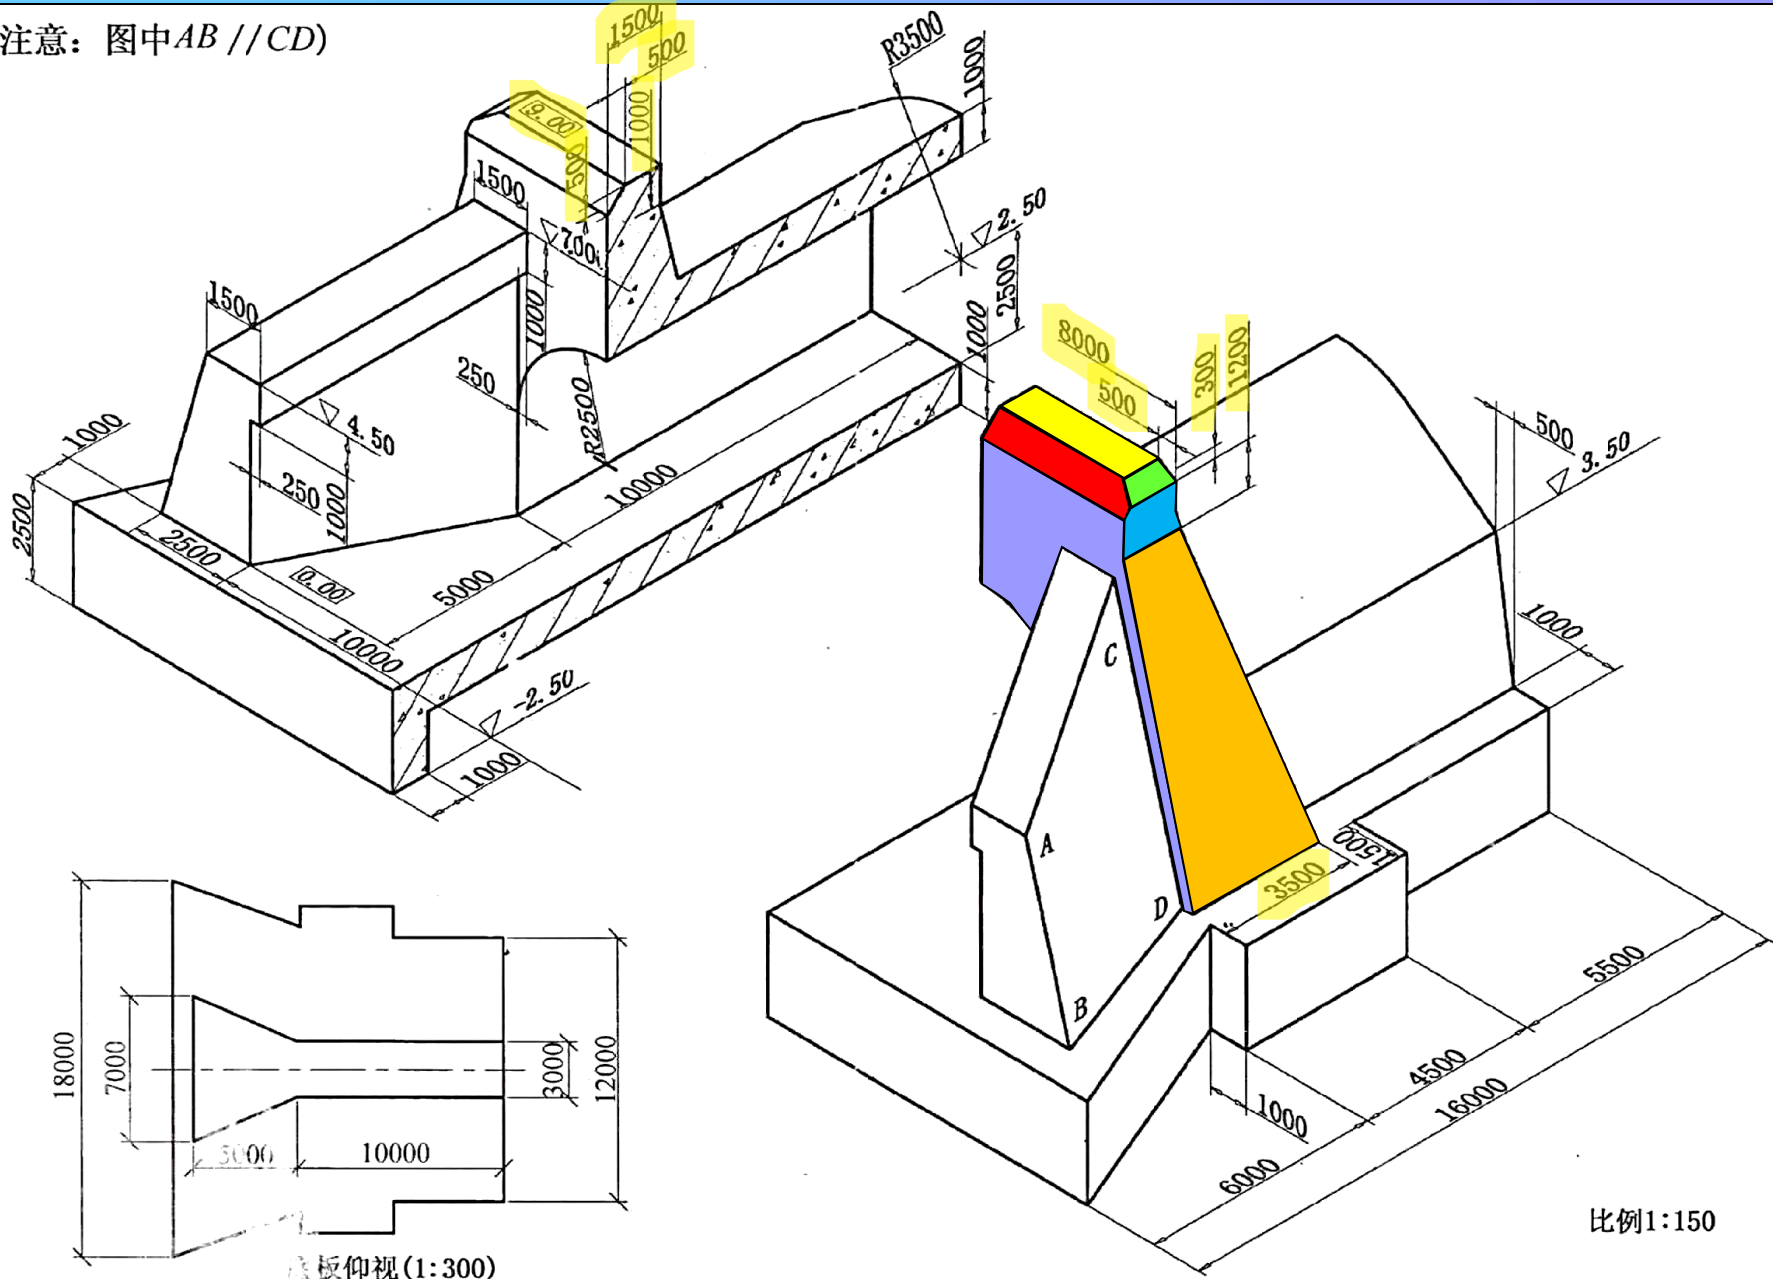

比例1:150


面墙倒角

注意：面墙顶面两端的倒角

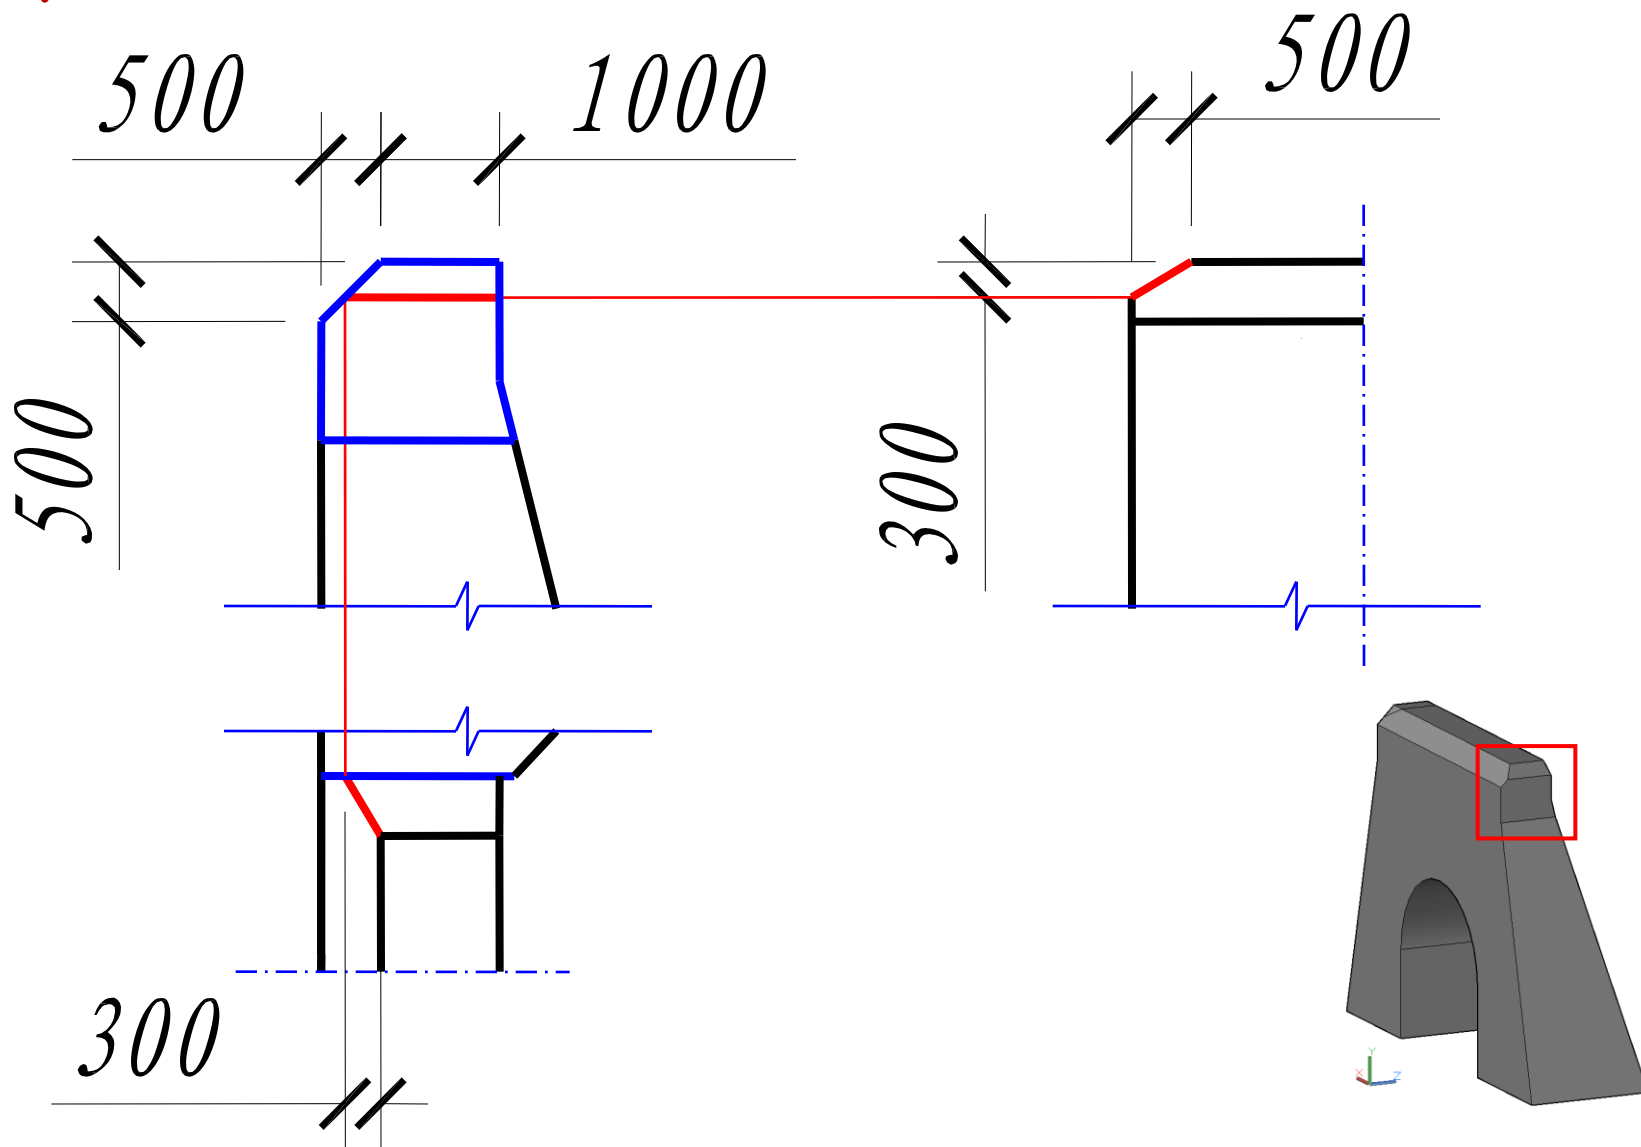


4、洞身

洞身由边墙和拱圈组成，位于底板之上，呈狭长形。其中间为拱形穿孔，供水流通过。

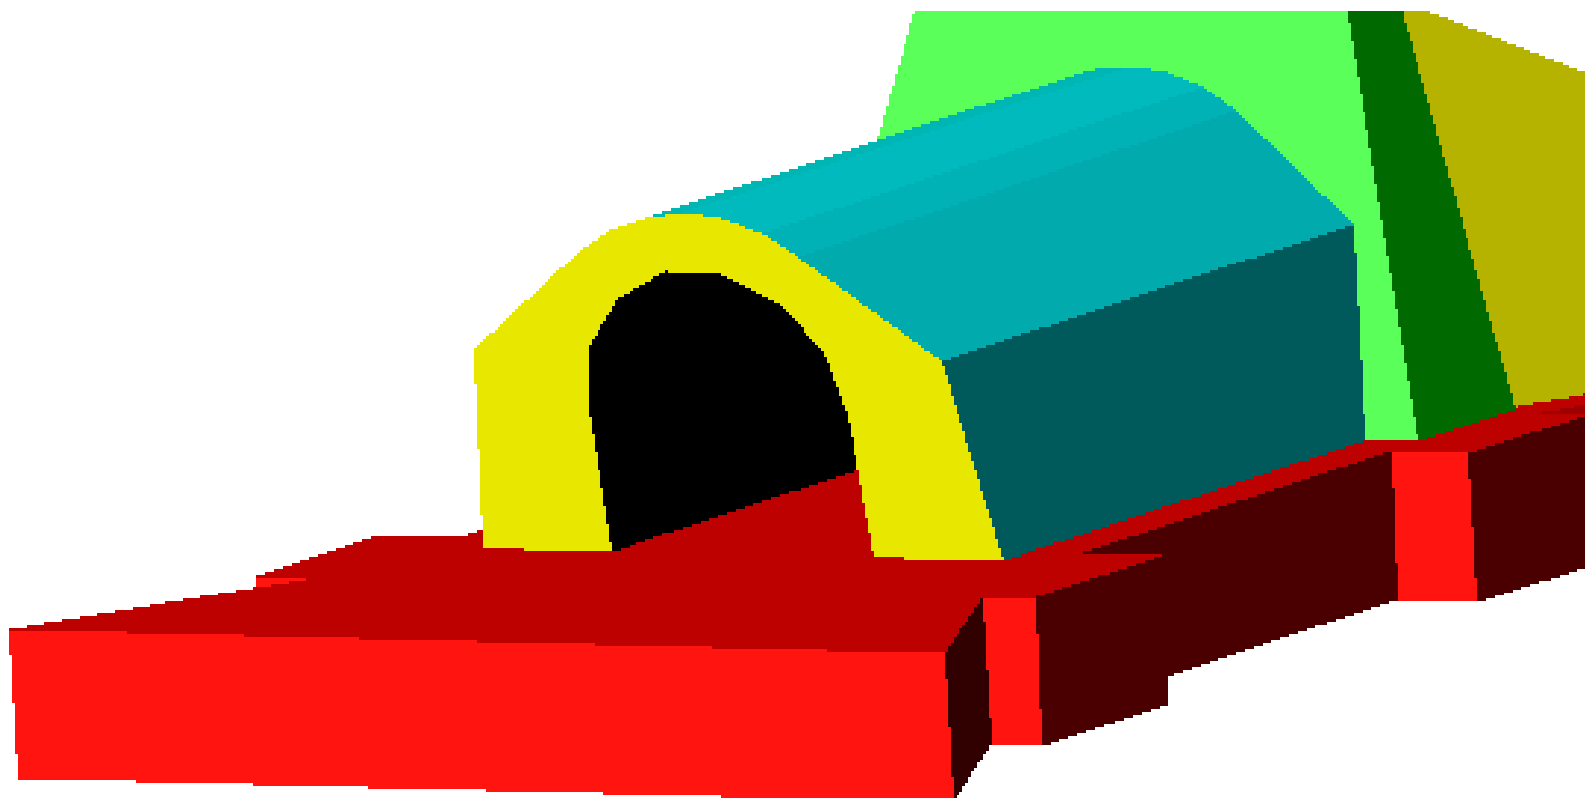

(注意: 图中 $AB \parallel CD$)

(注意: 图中 $AB \parallel CD$)

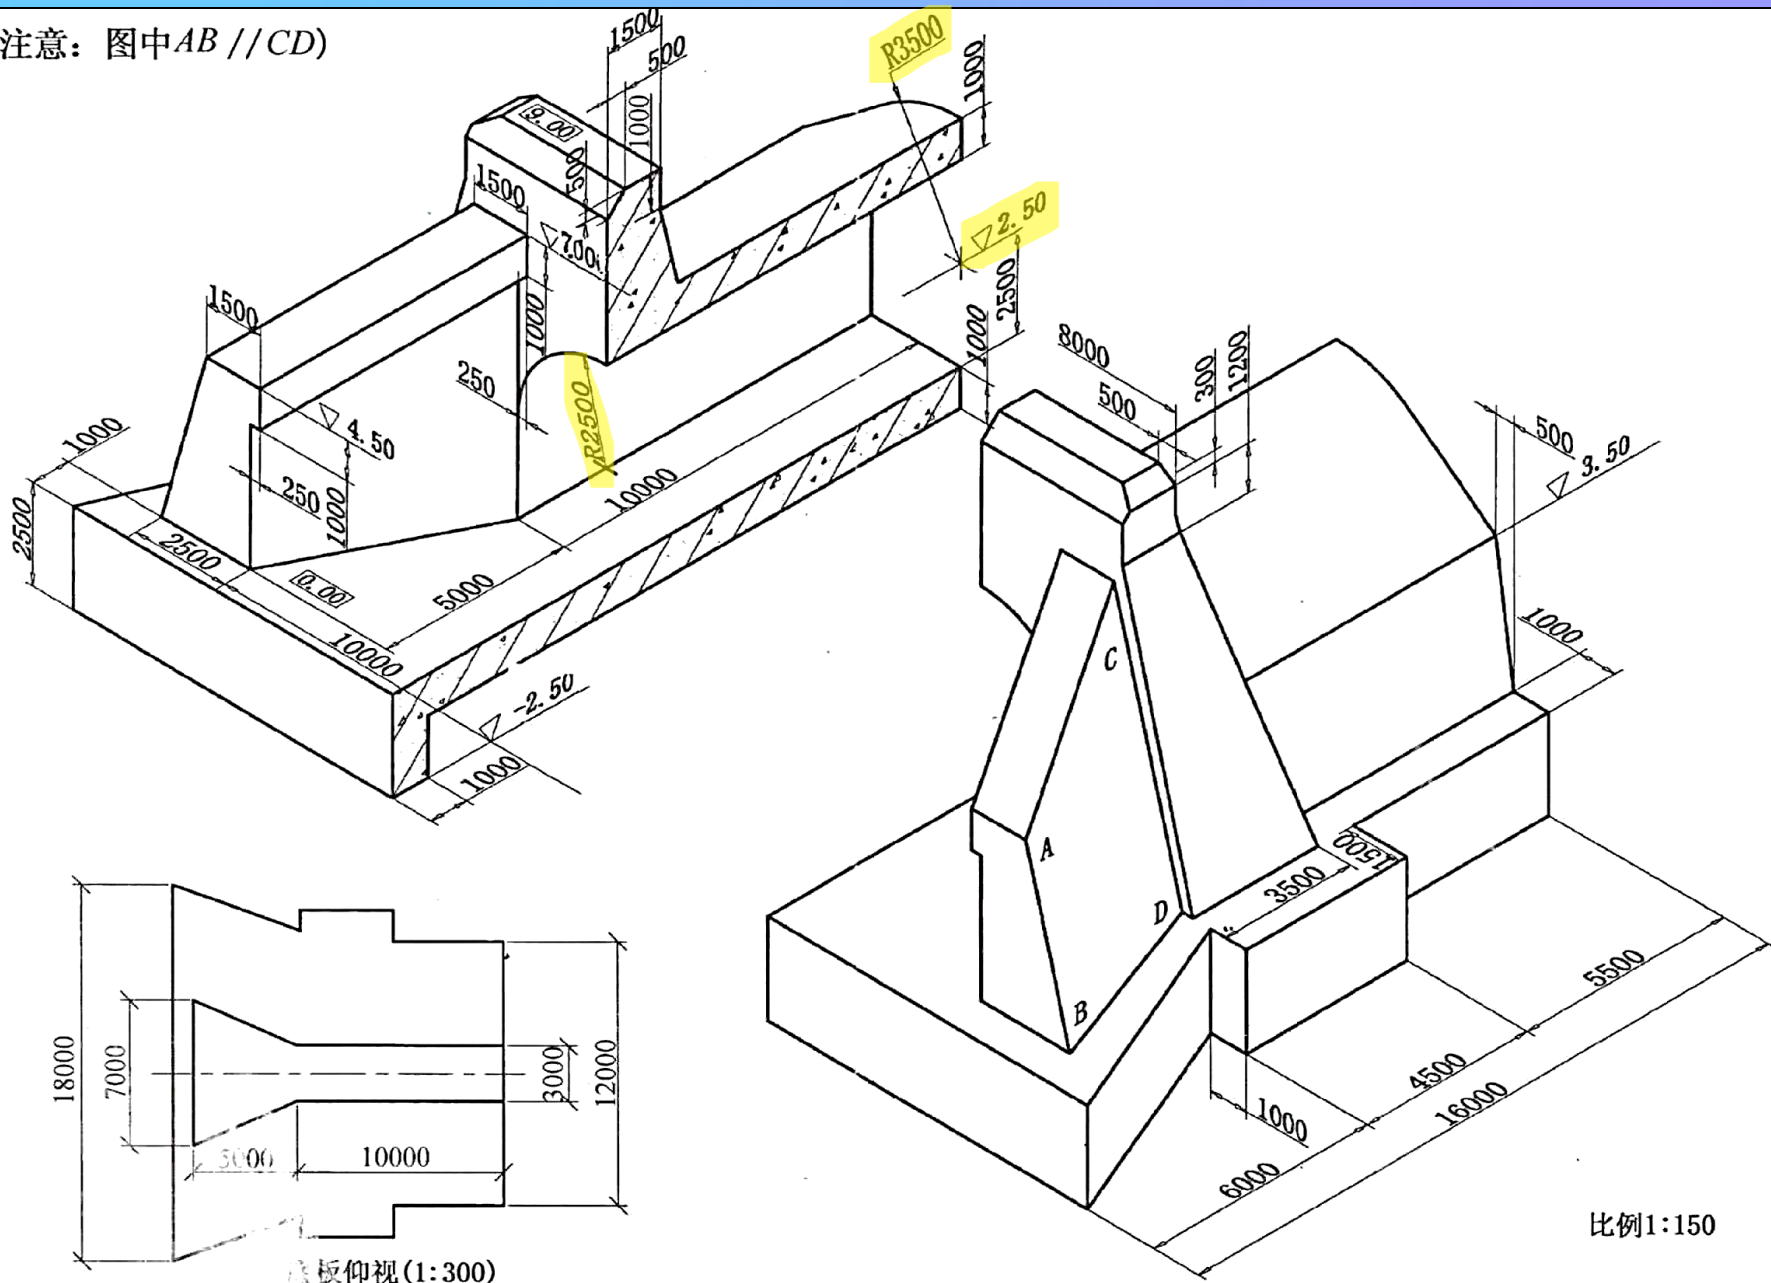

比例1:150